CHARLES RIVER PROVISIONS

120 LOWLAND ST | HOLLISTON, MA 01746

ELECTRICAL DISTRIBUTION

EXISTING SERVICE - CONCEPT REVIEW


UTILITY SERVICE

EVERSOURCE

SERVICE VOLTAGE: 480Y/277V

SYSTEM: 3 PHASE, 4 WIRE

SERVICE ID: VERIFY IN FIELD

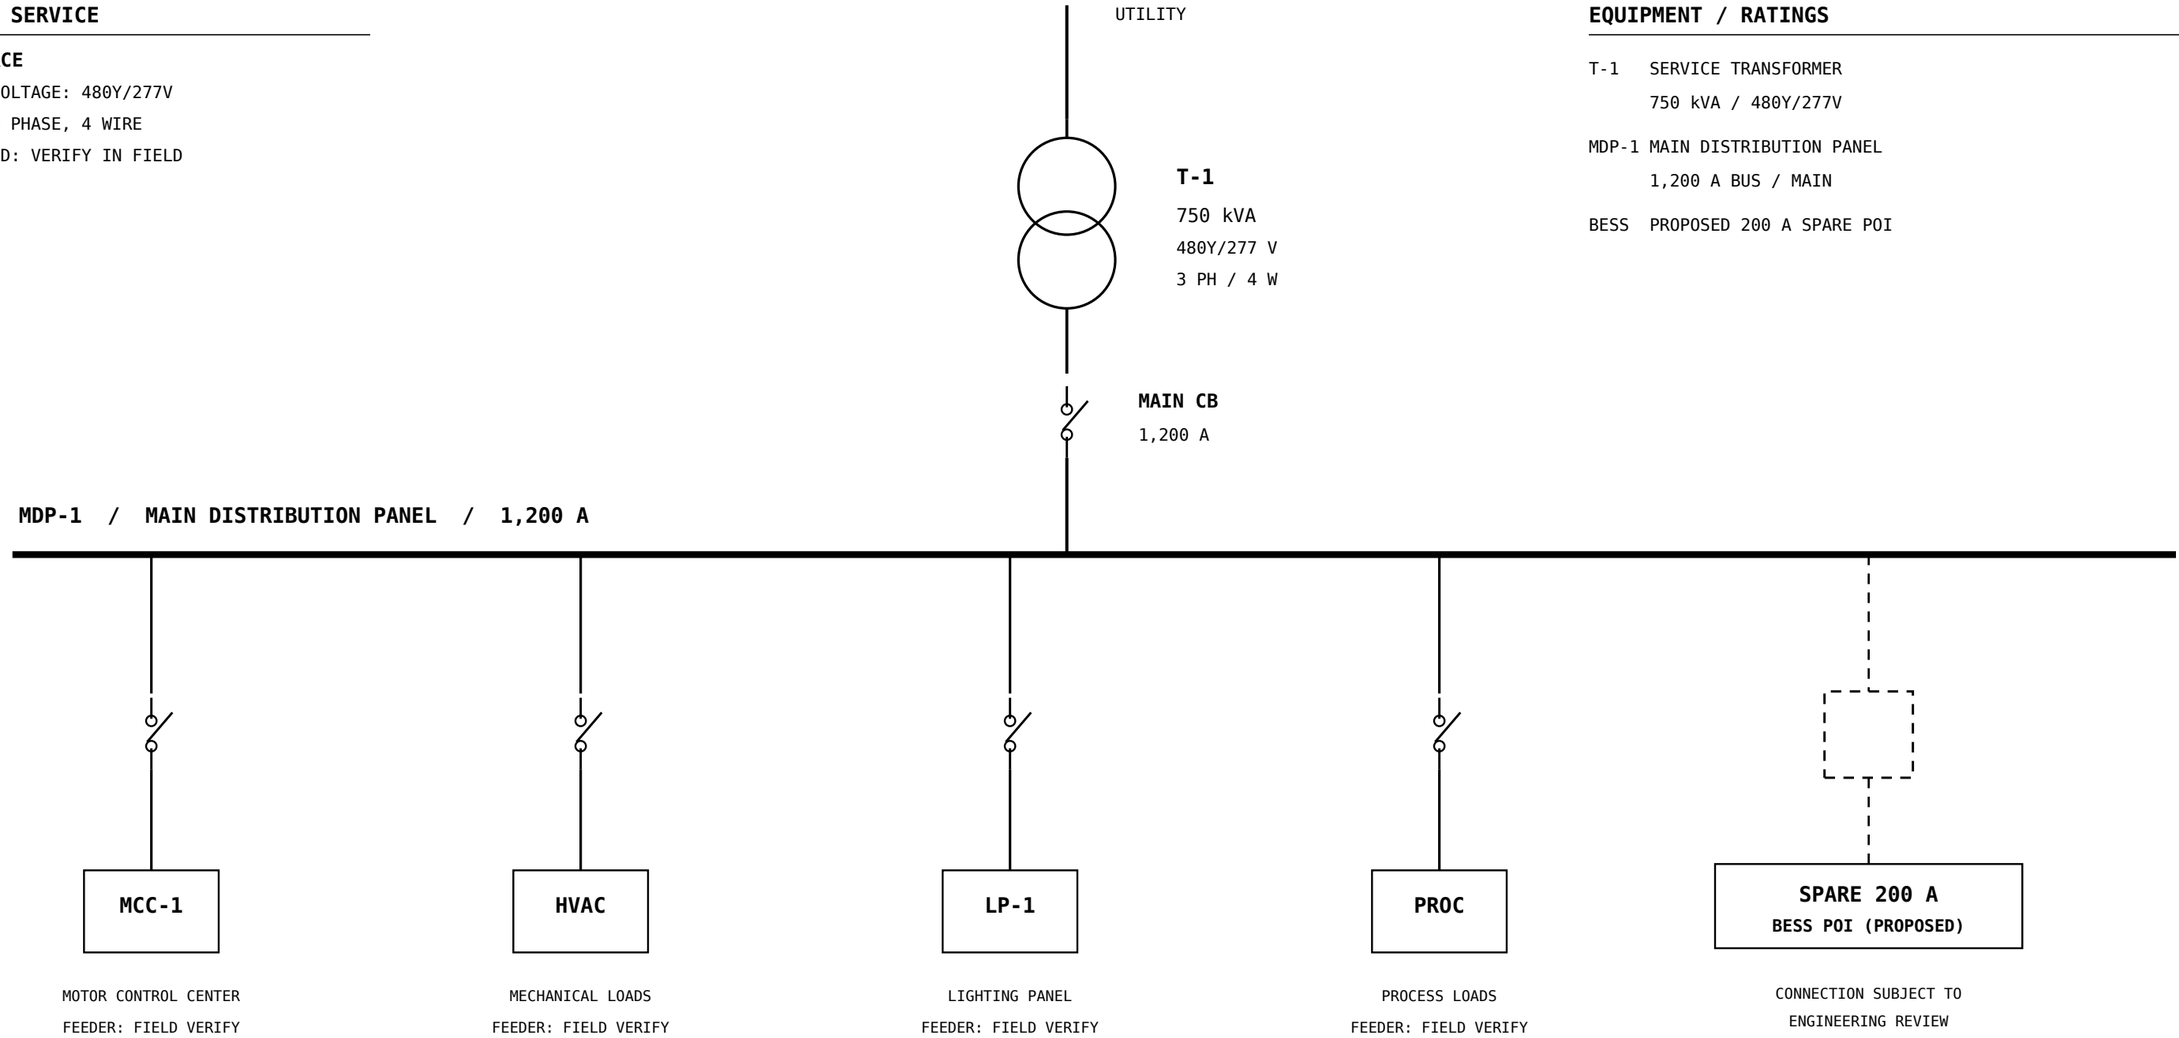

EQUIPMENT / RATINGS

T-1	SERVICE TRANSFORMER	750 kVA / 480Y/277V
MDP-1	MAIN DISTRIBUTION PANEL	1,200 A BUS / MAIN
BESS	PROPOSED 200 A SPARE POI	

SINGLE-LINE NOTES

1. EXISTING ELECTRICAL CONFIGURATION SHOWN FOR DEMONSTRATION PURPOSES ONLY.
2. FIELD VERIFY PROTECTIVE DEVICES, FEEDER SIZES, SHORT-CIRCUIT DUTY AND SPARE CAPACITY.

LEGEND

EXISTING

PROPOSED

DRAWING TITLE

ELECTRICAL SINGLE-LINE DIAGRAM

EXISTING SERVICE / PROPOSED BESS POI

PROJECT	REVISION	DRAWING NO.
CHARLES RIVER PROVISIONS	C	E-001
DEMO DOCUMENT - NOT FOR CONSTRUCTION	ISSUED 10/27/2026	SHEET 1 OF 1